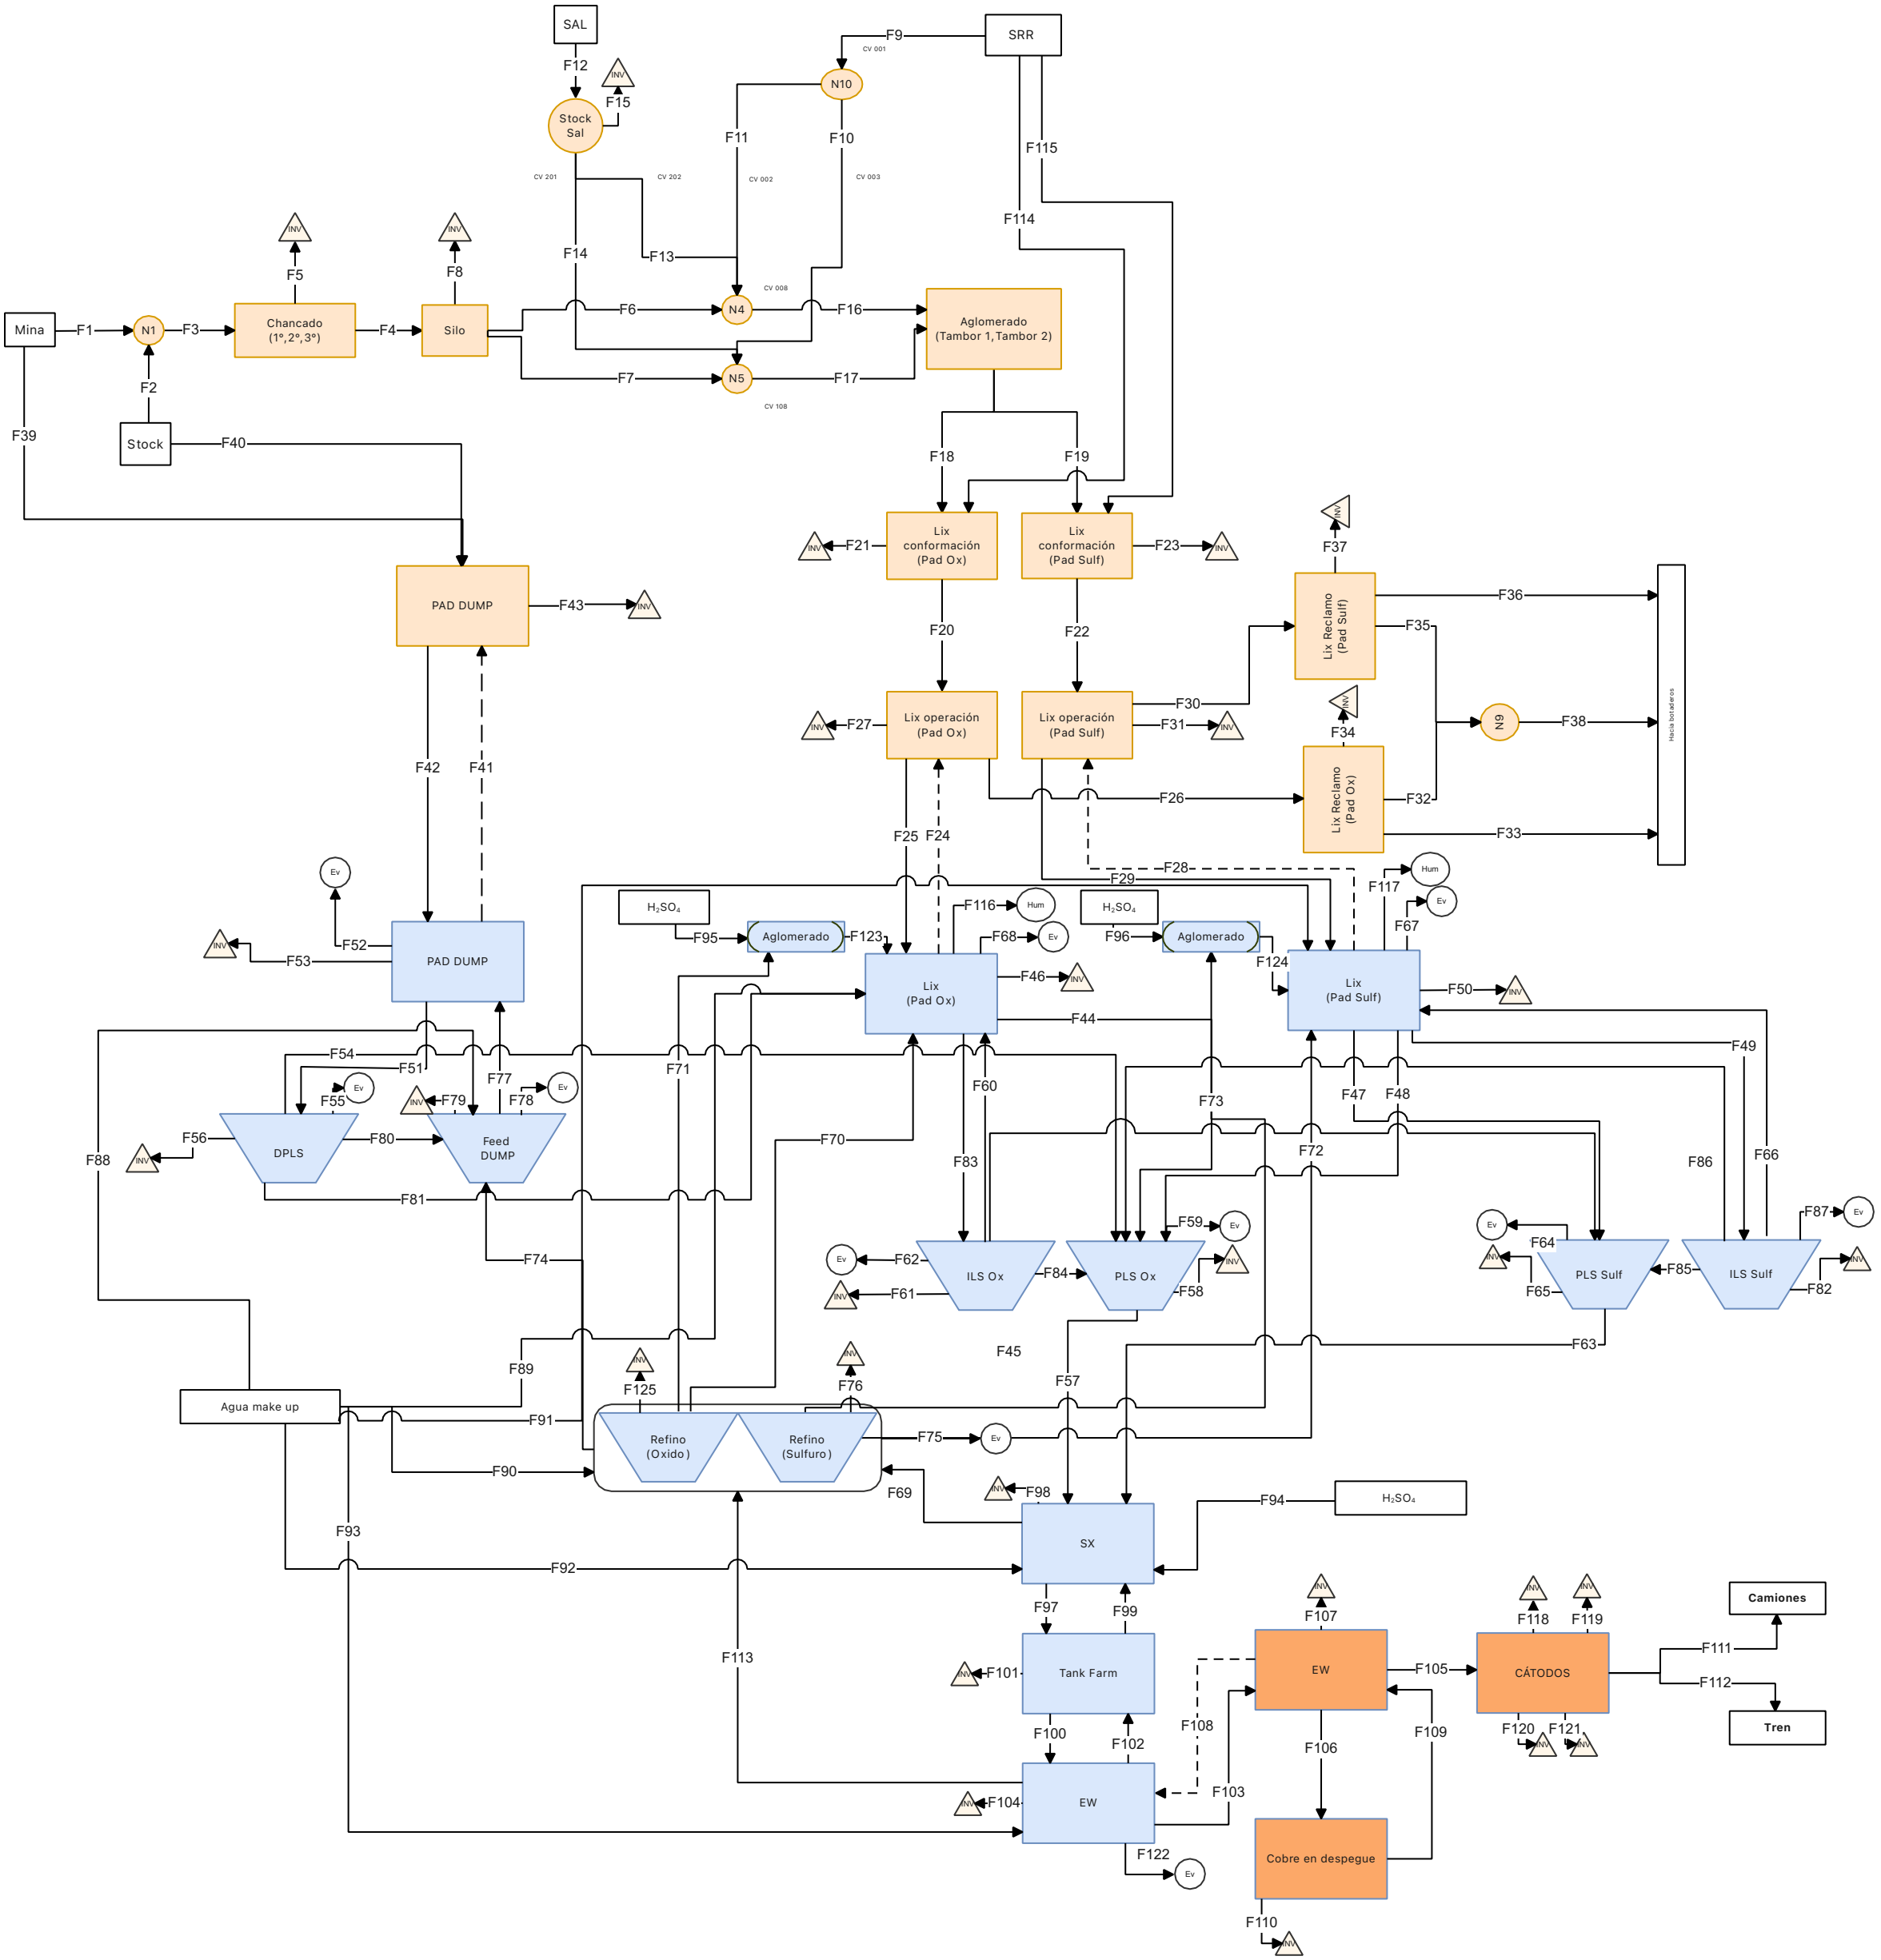

SAL
F12
F15
Stock Sal
F9
SRR
N10
F11
F10
F115
F114
CV 001
CV 201
CV 202
CV 002
CV 003
F14
F13
CV 008
Mina
F1
N1
F3
Chancado (1°,2°,3°)
F4
Silo
F6
N4
F16
Aglomerado (Tambor 1, Tambor 2)
F5
F8
F7
N5
F17
CV 108
F2
Stock
F40
F39
F18
F19
Lix conformación (Pad Ox)
Lix conformación (Pad Sulf)
F21
F23
F37
PAD DUMP
F43
F20
F22
Lix Reclamo (Pad Sulf)
F36
F35
Lix operación (Pad Ox)
Lix operación (Pad Sulf)
F27
F30
F31
F34
N6
F38
Hacia botaderos
F42
F41
F26
Lix Reclamo (Pad Ox)
F32
F33
F25
F24
F28
F29
Ev
F52
F53
PAD DUMP
H_2SO_4
F95
Aglomerado
F123
F116
Hum
F68
Ev
H_2SO_4
F96
Aglomerado
F124
F117
Hum
Ev
F67
Lix (Pad Ox)
F46
F44
Lix (Pad Sulf)
F50
F49
F54
F51
F77
F71
F60
F73
F47
F48
F55
Ev
F79
F78
Ev
DPLS
F80
Feed DUMP
F56
F70
F72
F88
F83
F86
F66
F81
F59
Ev
F87
Ev
F74
F62
Ev
ILS Ox
F84
PLS Ox
F64
Ev
F61
F58
PLS Sulf
F85
ILS Sulf
F65
F82
F63
F45
F89
F125
F76
F57
Agua make up
F91
Refino (Oxido)
Refino (Sulfuro)
F75
Ev
F90
F69
F98
F94
H_2SO_4
F93
SX
F92
F97
F99
F107
F118
F119
Camiones
F111
F113
F101
Tank Farm
EW
F105
CÁTODOS
F112
F108
F100
F102
F106
F109
F120
F121
Tren
F104
EW
F103
F122
Ev
Cobre en despegue
F110