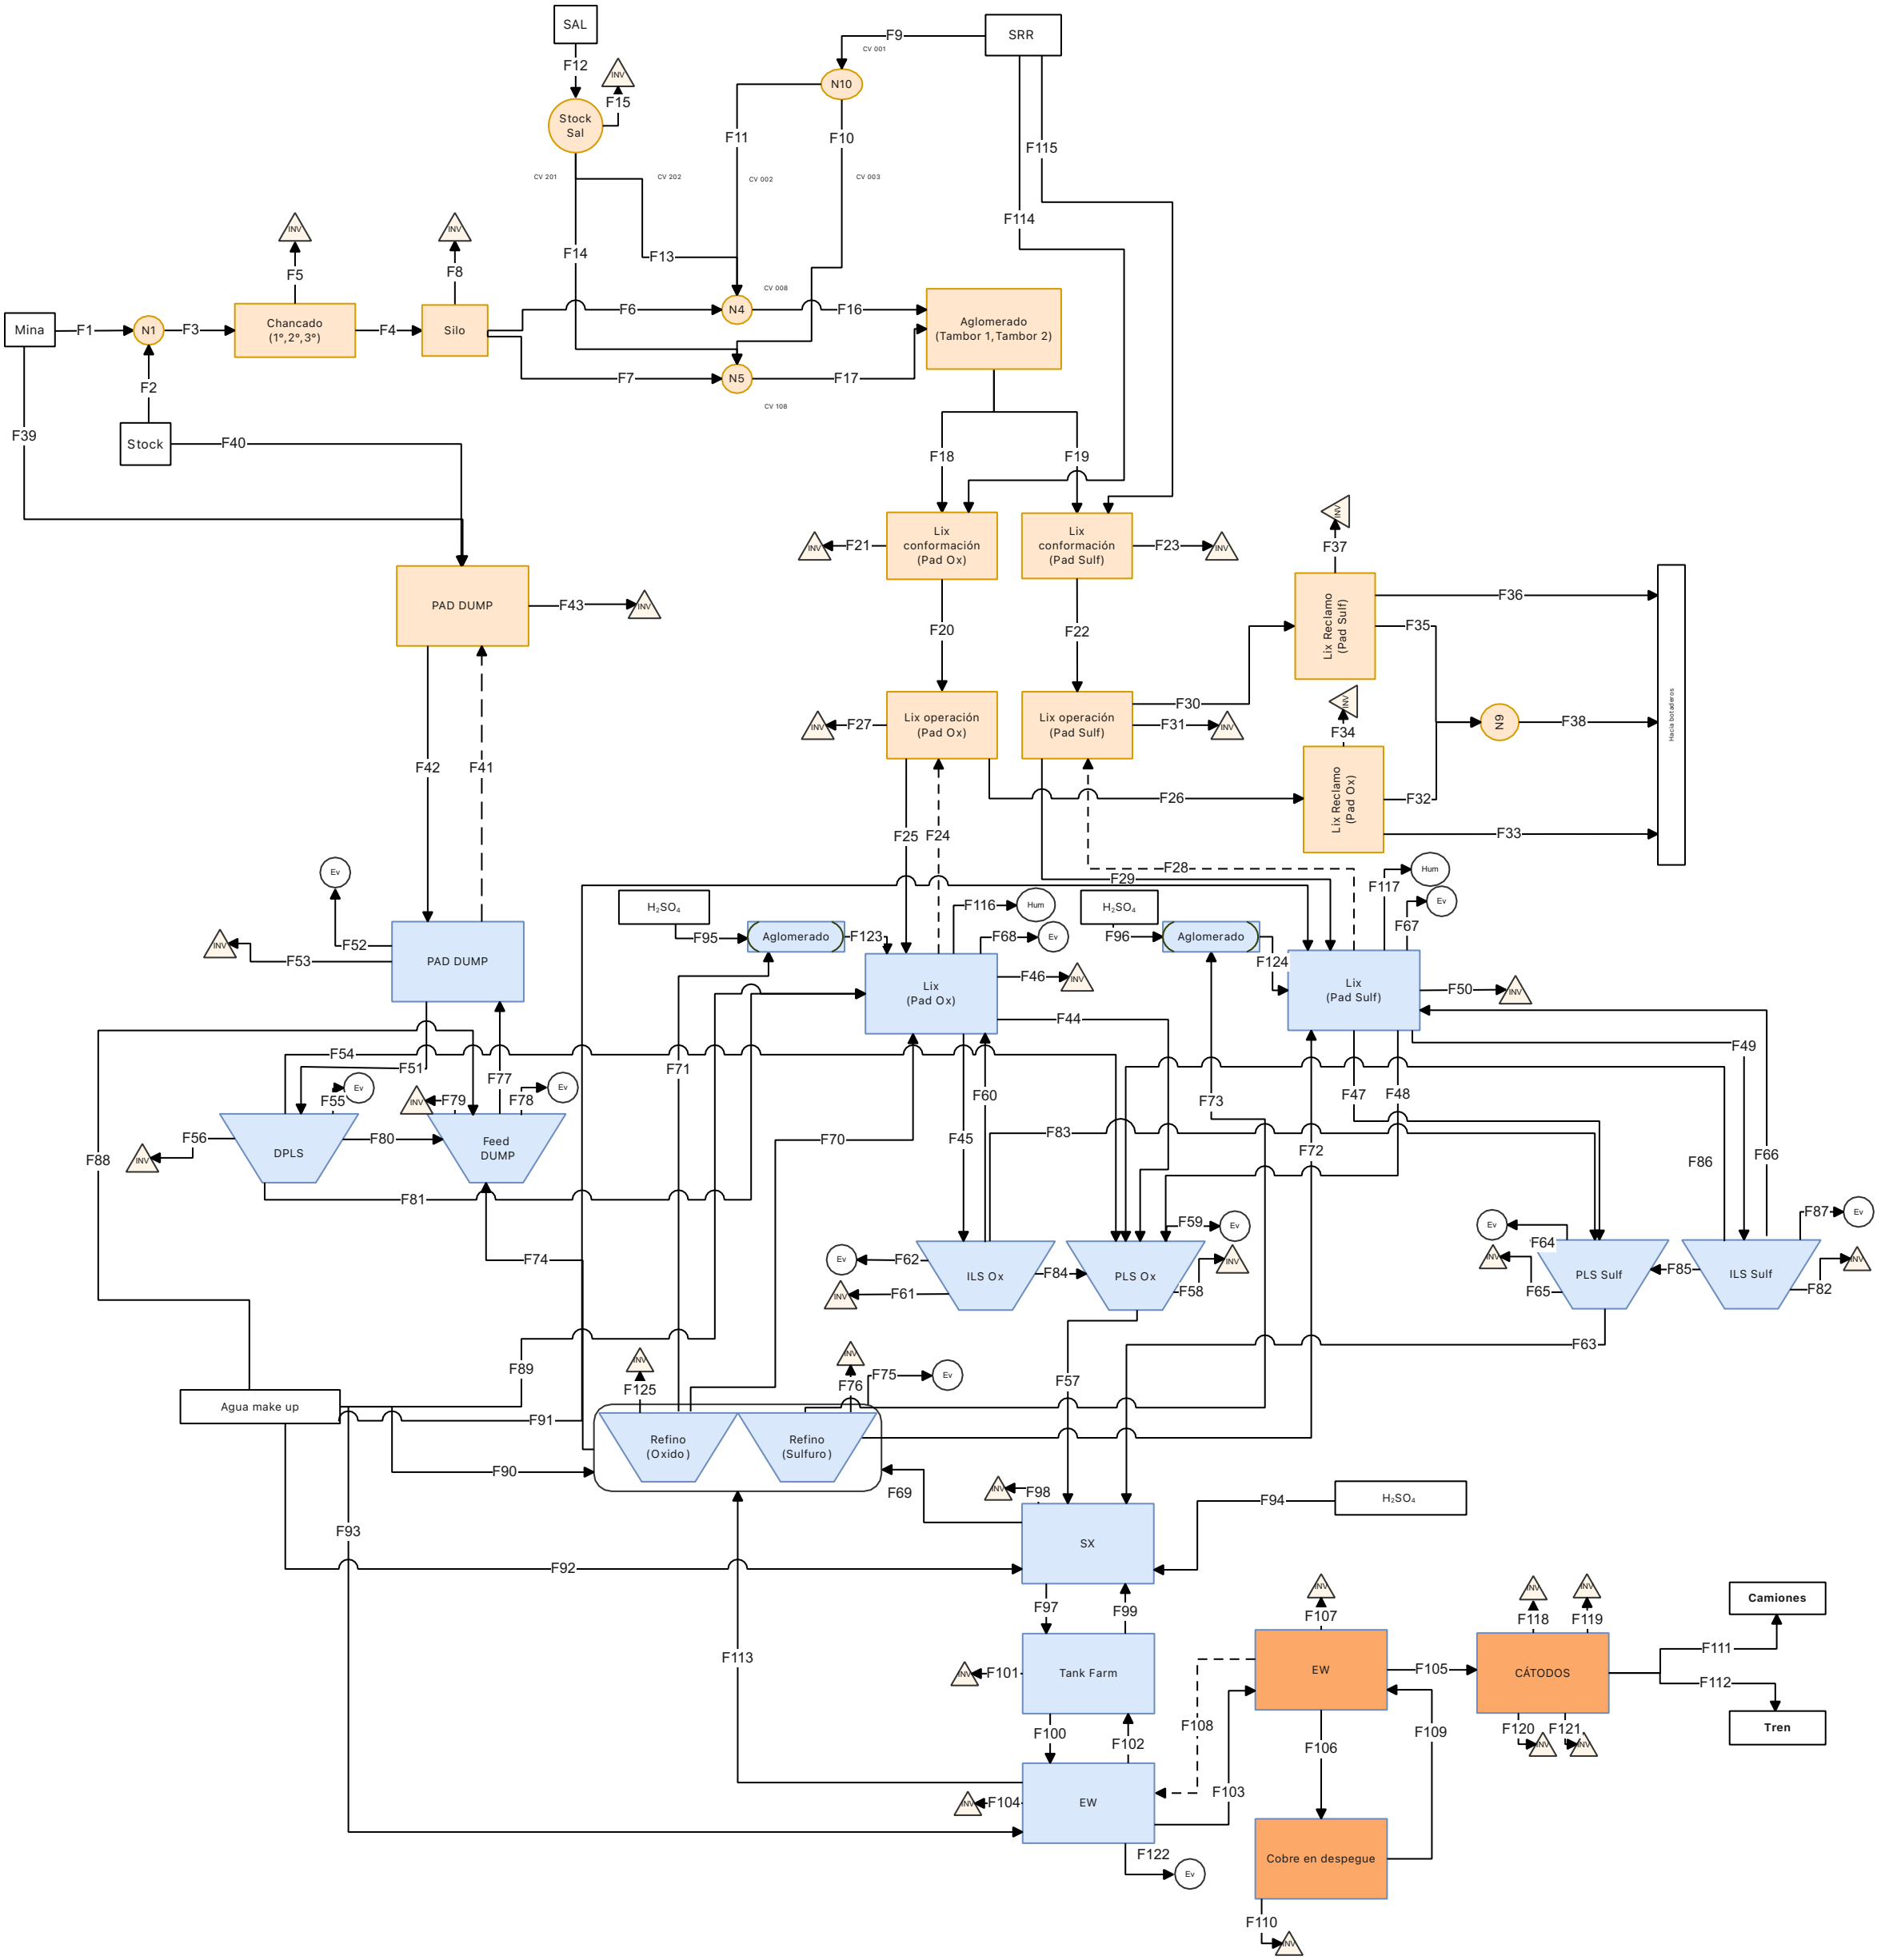

SAL
F12
INV
F15
Stock Sal
F9
CV 001
SRR
N10
F11
F10
F115
CV 201
CV 202
CV 002
CV 003
F114
F14
F13
F5
F8
INV
INV
Mina
F1
N1
F3
Chancado (1°,2°,3°)
F4
Silo
F6
N4
CV 008
F16
Aglomerado (Tambor 1, Tambor 2)
F7
N5
F17
CV 108
F2
Stock
F40
F39
F18
F19
PAD DUMP
F43
INV
Lix conformación (Pad Ox)
Lix conformación (Pad Sulf)
INV
F21
F23
INV
F37
INV
Lix Reclamo (Pad Sulf)
F36
F35
F20
F22
Lix operación (Pad Ox)
Lix operación (Pad Sulf)
F30
F27
F31
INV
INV
F34
INV
N6
F38
Hacia botaderos
F42
F41
Lix Reclamo (Pad Ox)
F32
F26
F33
F25
F24
F28
F29
Ev
F117
Hum
Ev
F67
H2SO4
F95
Aglomerado
F123
F116
Hum
Ev
F68
H2SO4
F96
Aglomerado
F124
Lix (Pad Ox)
F46
INV
Lix (Pad Sulf)
F50
INV
F44
F49
F52
INV
F53
PAD DUMP
F54
F51
F71
F77
F78
Ev
F55
Ev
INV
F79
F60
F73
F47
F48
F56
DPLS
F80
Feed DUMP
F70
F45
F83
F72
F86
F66
F88
INV
F81
F74
Ev
F62
INV
F61
ILS Ox
F84
PLS Ox
F59
Ev
INV
F58
Ev
INV
F64
PLS Sulf
F85
ILS Sulf
F87
Ev
INV
F82
F65
F63
F89
INV
F125
INV
F76
F75
Ev
F57
Agua make up
F91
Refino (Oxido)
Refino (Sulfuro)
F90
F69
INV
F98
F94
H2SO4
F93
SX
F92
F97
F99
F107
INV
F118
INV
F119
INV
Camiones
F113
Tank Farm
INV
F101
EW
F105
CÁTODOS
F111
F112
F100
F102
F108
F109
F106
F120
INV
F121
INV
Tren
INV
F104
EW
F103
F122
Ev
Cobre en despegue
F110
INV